SENSITIVE AREAS EXHIBIT
HIDDEN LAKES
JOHNSON COUNTY, IOWA

PLAT PREPARED BY:
MMS CONSULTANTS INC.
1917 S. GILBERT STREET
IOWA CITY, IA 52240

OWNER:
HIDDEN LAKES LLC
4105 WESTCOR CT #2
CORALVILLE, IA 52241

APPLICANT:
KLOSTERMAN CONSTRUCTION
P.O. BOX 2575
CORALVILLE, IA 52241

APPLICANT'S ATTORNEY:
RYAN PRAHM
425 E OASKDALE BLVD SUITE 201
CORALVILLE, IA 52241

NORTH
0 8 20 40 60 80
GRAPHIC SCALE IN FEET
1"=80'

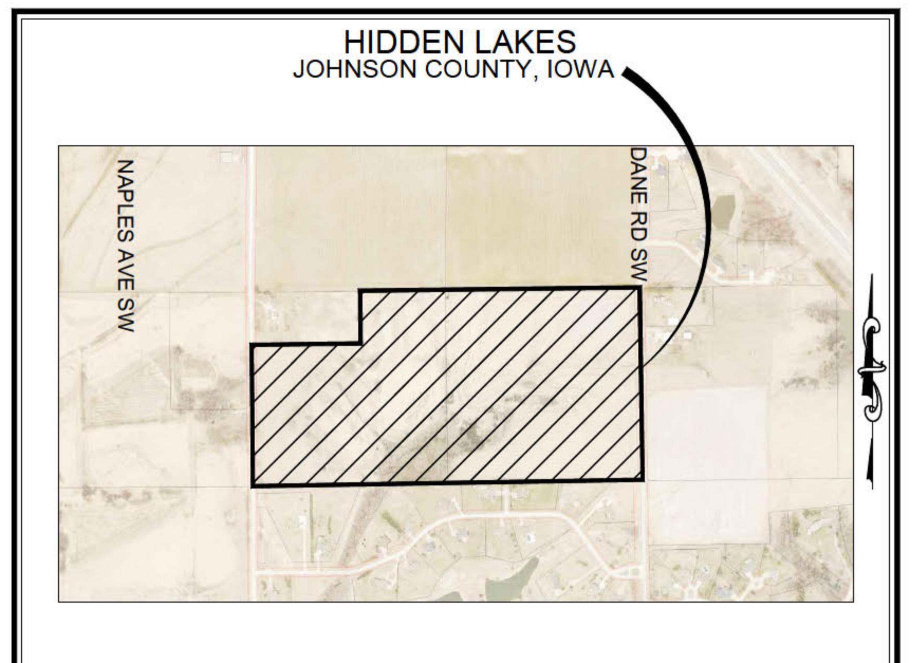

LOCATION MAP
NOT TO SCALE

SENSITIVE AREAS LEGEND

- STREAM CORRIDORS (669 LINEAR FEET)
- WATERCOURSE (296 LINEAR FEET)
- 30' STREAM CORRIDOR/ WATERCOURSE BUFFER
- CLASS 3 WETLANDS (0.67 ACRES)
- 50' WETLAND BUFFER
- SENSITIVE WOODLAND (4.32 ACRES)
- 50' WOODLAND BUFFER
- LIMITS OF DISTURBANCE
- CONSERVATION EASEMENT
- INTERMITTENT STREAM (WATERCOURSE) IMPACT (209 LINEAR FEET)
- PERENNIAL STREAM (STREAM CORRIDOR) IMPACT (81 LINEAR FEET)
- WETLAND IMPACT (0.19 ACRES OR 28.36%)
- *WOODLAND IMPACT 1.05 ACRES or 24.31%

*0.47 ACRES GENERAL DEVELOPMENT 10.88%

*0.58 ACRES STORMWATER MANAGEMENT 13.43%

SENSITIVE AREAS NOTES

1. A CONSERVATION EASEMENT HAS BEEN ESTABLISHED TO PROTECT SENSITIVE AREAS AND ASSOCIATED BUFFERS. PLEASE REFER TO THE CONSERVATION EASEMENT AGREEMENT RECORDED WITH THIS SUBDIVISION FOR A LIST OF ALLOWED AND PROHIBITED USES WITHIN THE CONSERVATION EASEMENT.
2. THE CONSERVATION EASEMENT SHALL BE FLAGGED ON SITE PRIOR TO ANY CONSTRUCTION ACTIVITIES. AN ONSITE PRE-CONSTRUCTION MEETING SHALL BE HELD PRIOR TO THE COMMENCEMENT OF ANY GROUND DISTURBING ACTIVITIES.
3. A SURVEY OF THE ACTUAL IMPACT BOUNDARY AND CALCULATED IMPACT AREA SHALL BE SUBMITTED TO JOHNSON COUNTY PRIOR TO RECEIVING FINAL PLAT APPROVAL.
4. PRIOR APPROVAL FROM THE COUNTY IS REQUIRED FOR ANY MODIFICATION TO THE CONSERVATION EASEMENT.

5 COLOR VERSIONS OF THIS EXHIBIT ARE AVAILABLE ON FILE AT JOHNSON COUNTY PDS, ALONG WITH THE ACCOMPANYING SENSITIVE AREAS REPORT.

STANDARD LEGEND AND NOTES

- PROPERTY &/or BOUNDARY LINES
- CONGRESSIONAL SECTION LINES
- RIGHT-OF-WAY LINES
- EXISTING RIGHT-OF-WAY LINES
- CENTER LINES
- EXISTING CENTER LINES
- LOT LINES, INTERNAL
- LOT LINES, PLATTED OR BY DEED
- PROPOSED EASEMENT LINES
- EXISTING EASEMENT LINES
- PROPOSED BUILDING SETBACK
- BENCHMARK
- (R) RECORDED DIMENSIONS
- 22-1 CURVE SEGMENT NUMBER

-EXIST- -PROP-

- POWER POLE
- POWER POLE W/DROP
- POWER POLE W/TRANS
- POWER POLE W/LIGHT
- GUY POLE
- LIGHT POLE
- SANITARY MANHOLE
- FIRE HYDRANT
- WATER VALVE
- DRAINAGE MANHOLE
- CURB INLET
- FENCE LINE
- EXISTING SANITARY SEWER
- PROPOSED SANITARY SEWER
- EXISTING STORM SEWER
- PROPOSED STORM SEWER
- WATER LINES
- ELECTRICAL LINES
- TELEPHONE LINES
- GAS LINES
- FIBER OPTIC
- OVERHEAD ELECTRIC
- CONTOUR LINES (2' INTERVAL)
- PROPOSED GROUND (2' INTERVAL)
- EXISTING TREE LINE
- EXISTING DECIDUOUS TREE & SHRUB
- EXISTING EVERGREEN TREES & SHRUBS

THE ACTUAL SIZE AND LOCATION OF ALL PROPOSED FACILITIES SHALL BE VERIFIED WITH CONSTRUCTION DOCUMENTS, WHICH ARE TO BE PREPARED AND SUBMITTED SUBSEQUENT TO THE APPROVAL OF THIS DOCUMENT.

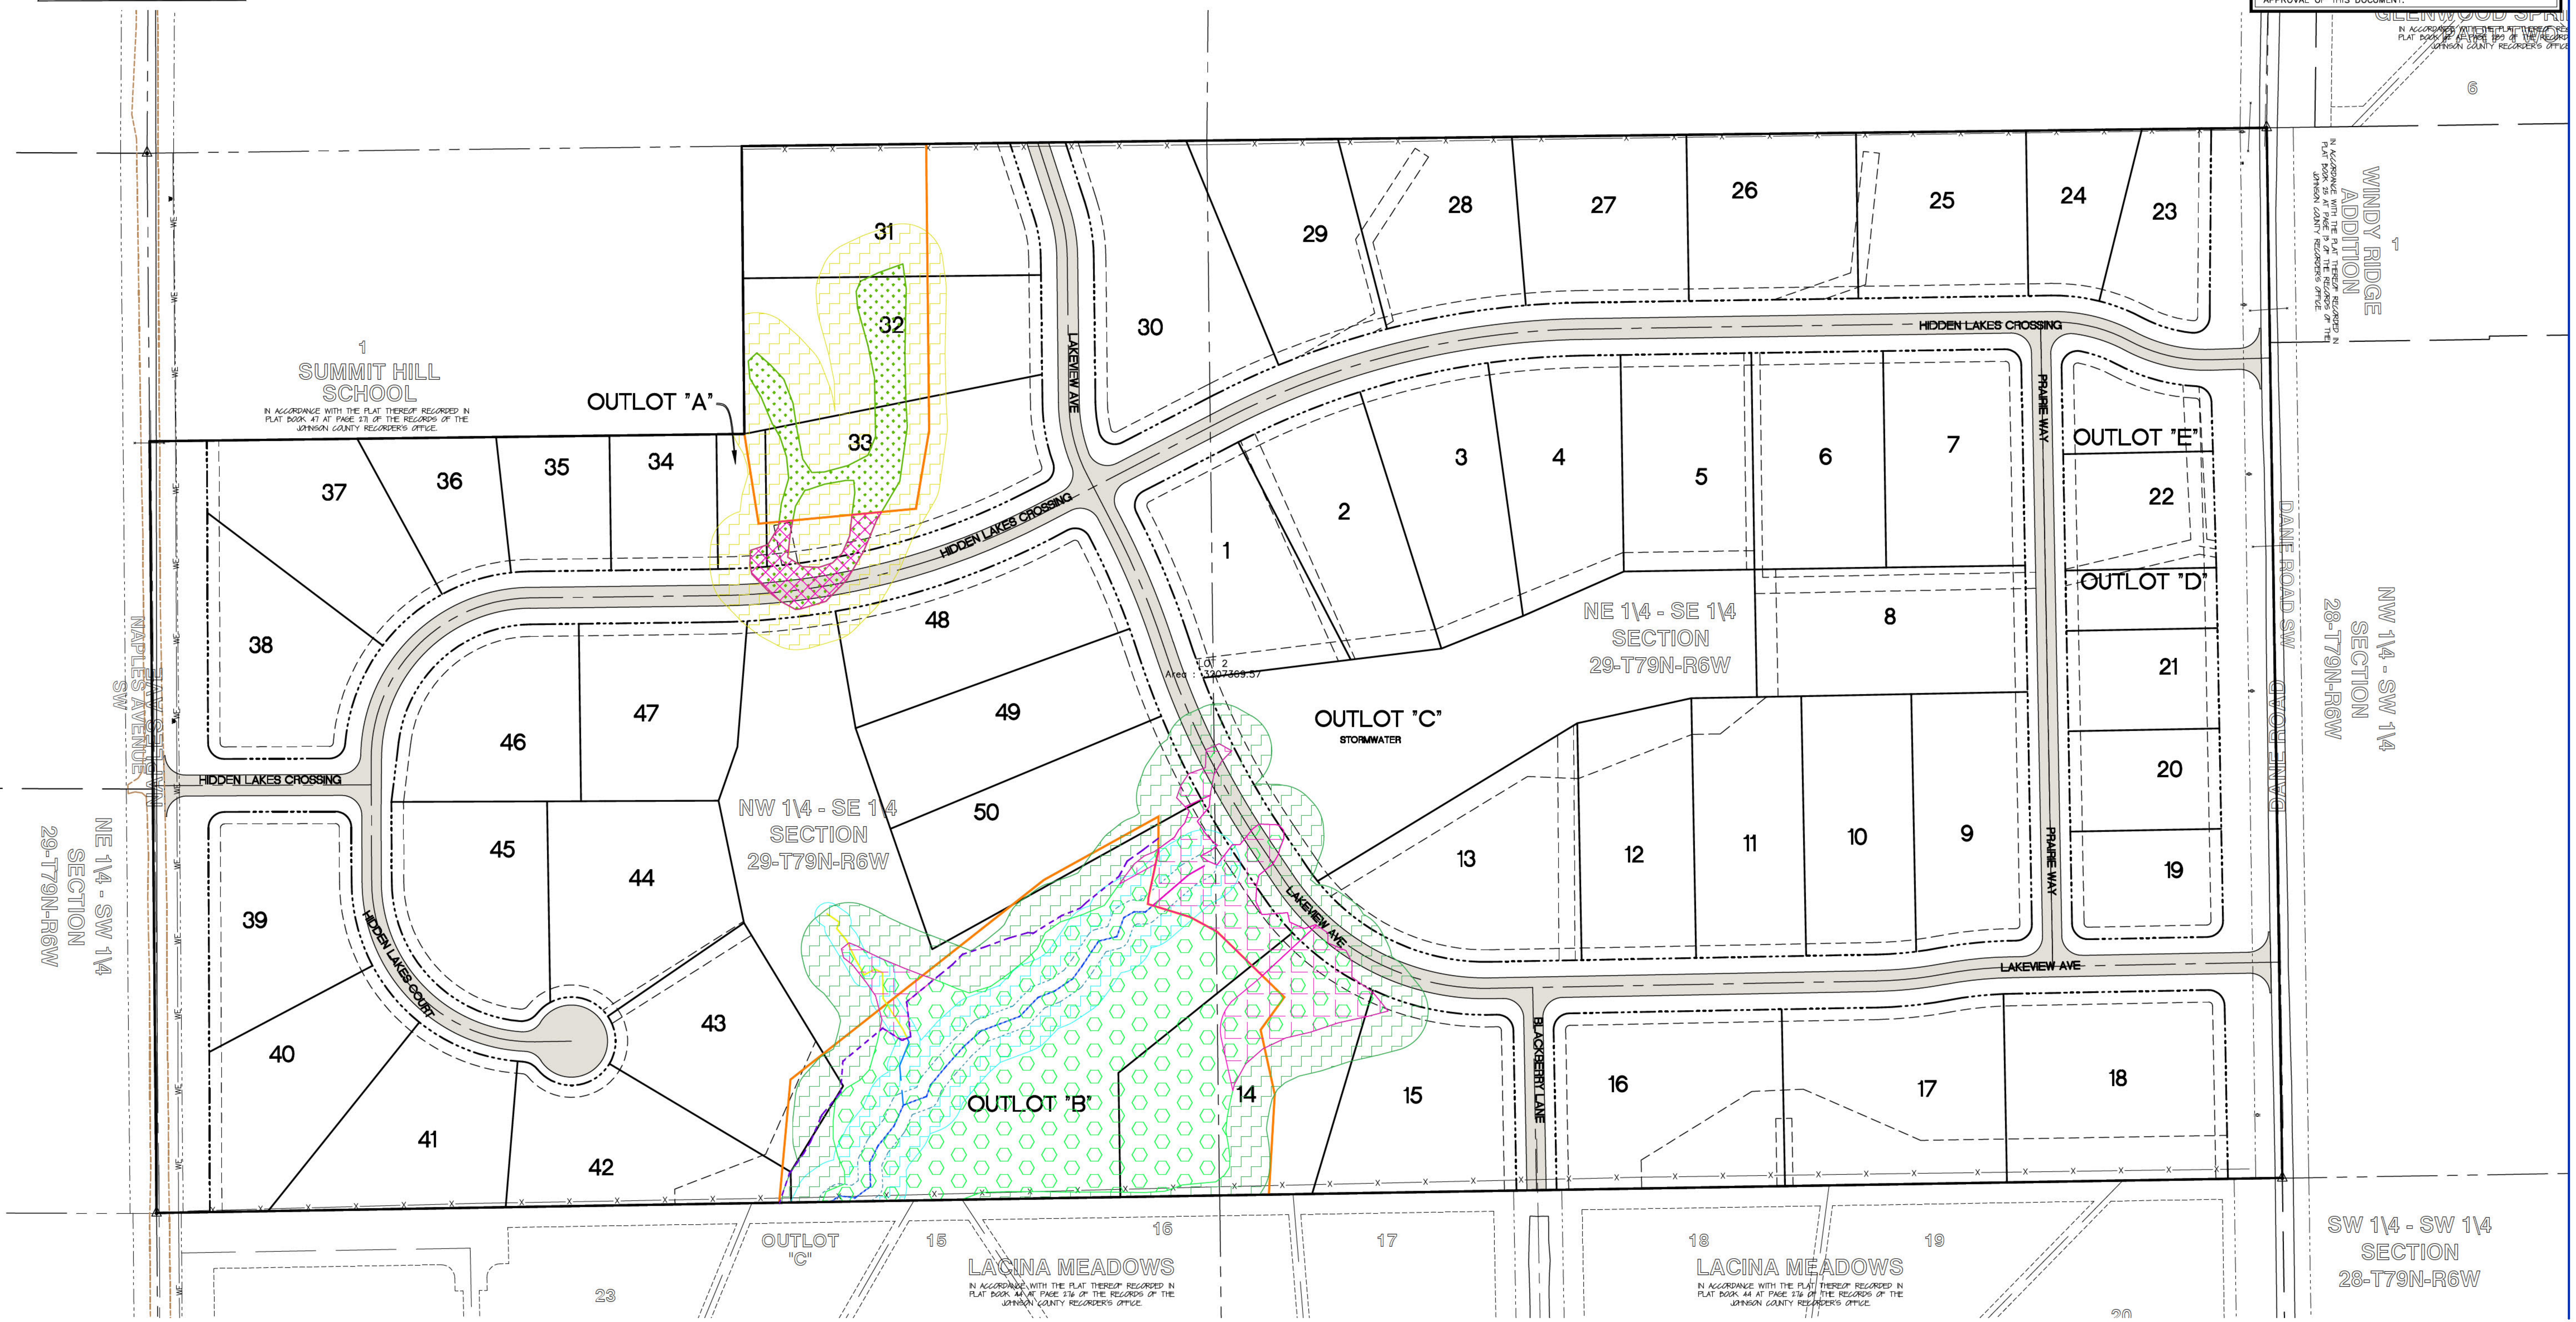

73.63 AC

CIVIL ENGINEERS
LAND PLANNERS
LAND SURVEYORS
LANDSCAPE ARCHITECTS
ENVIRONMENTAL SPECIALISTS

1917 S. GILBERT ST.
IOWA CITY, IOWA 52240
(319) 351-8282
www.mmsconsultants.net

Date	Revision

SENSITIVE AREAS EXHIBIT

HIDDEN LAKES

JOHNSON COUNTY IOWA

MMS CONSULTANTS, INC.

Date: 04/01/2025	
Designed by: RLA	Field Book No:
Drawn by: LRS	Scale: 1"=100'
Checked by: RLA	Sheet No: 1
Project No: 8231-026	of: 1